


CONSOLIDAMENTO PARETI PIANO TERRA

SCALA 1:20

PARETI ESTERNE

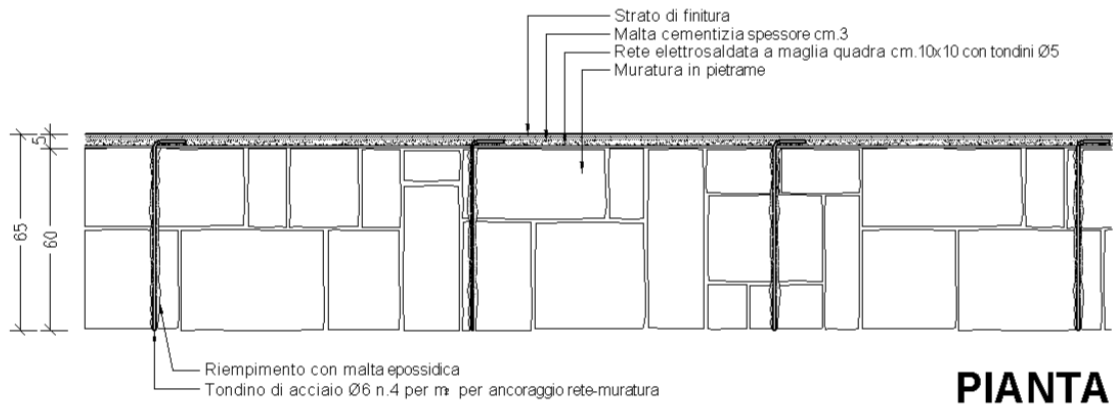

PARETI INTERNE

