


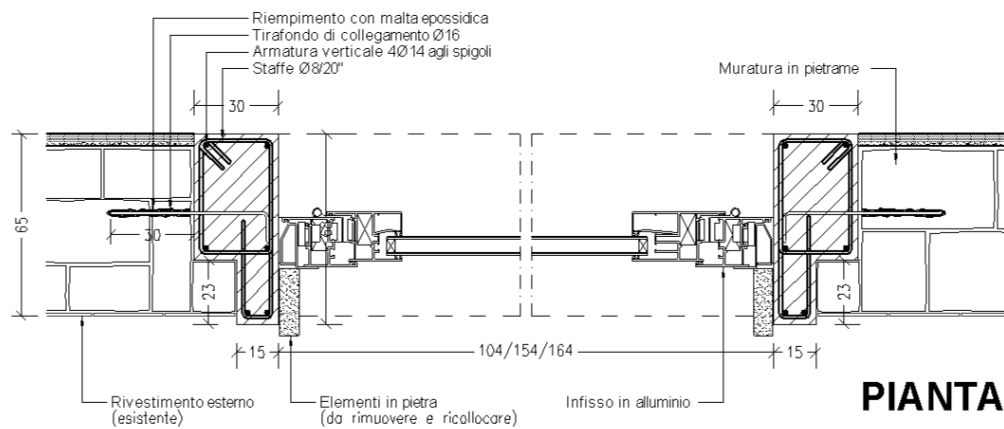

CONSOLIDAMENTO APERTURE MURATURE PIANO TERRA

SCALA 1:10

